Building B Floor 1 :
Department 3


Key :

3000 Code = Engineering Department

= Support Cubicle

= Regular Cubicle

Floor 1

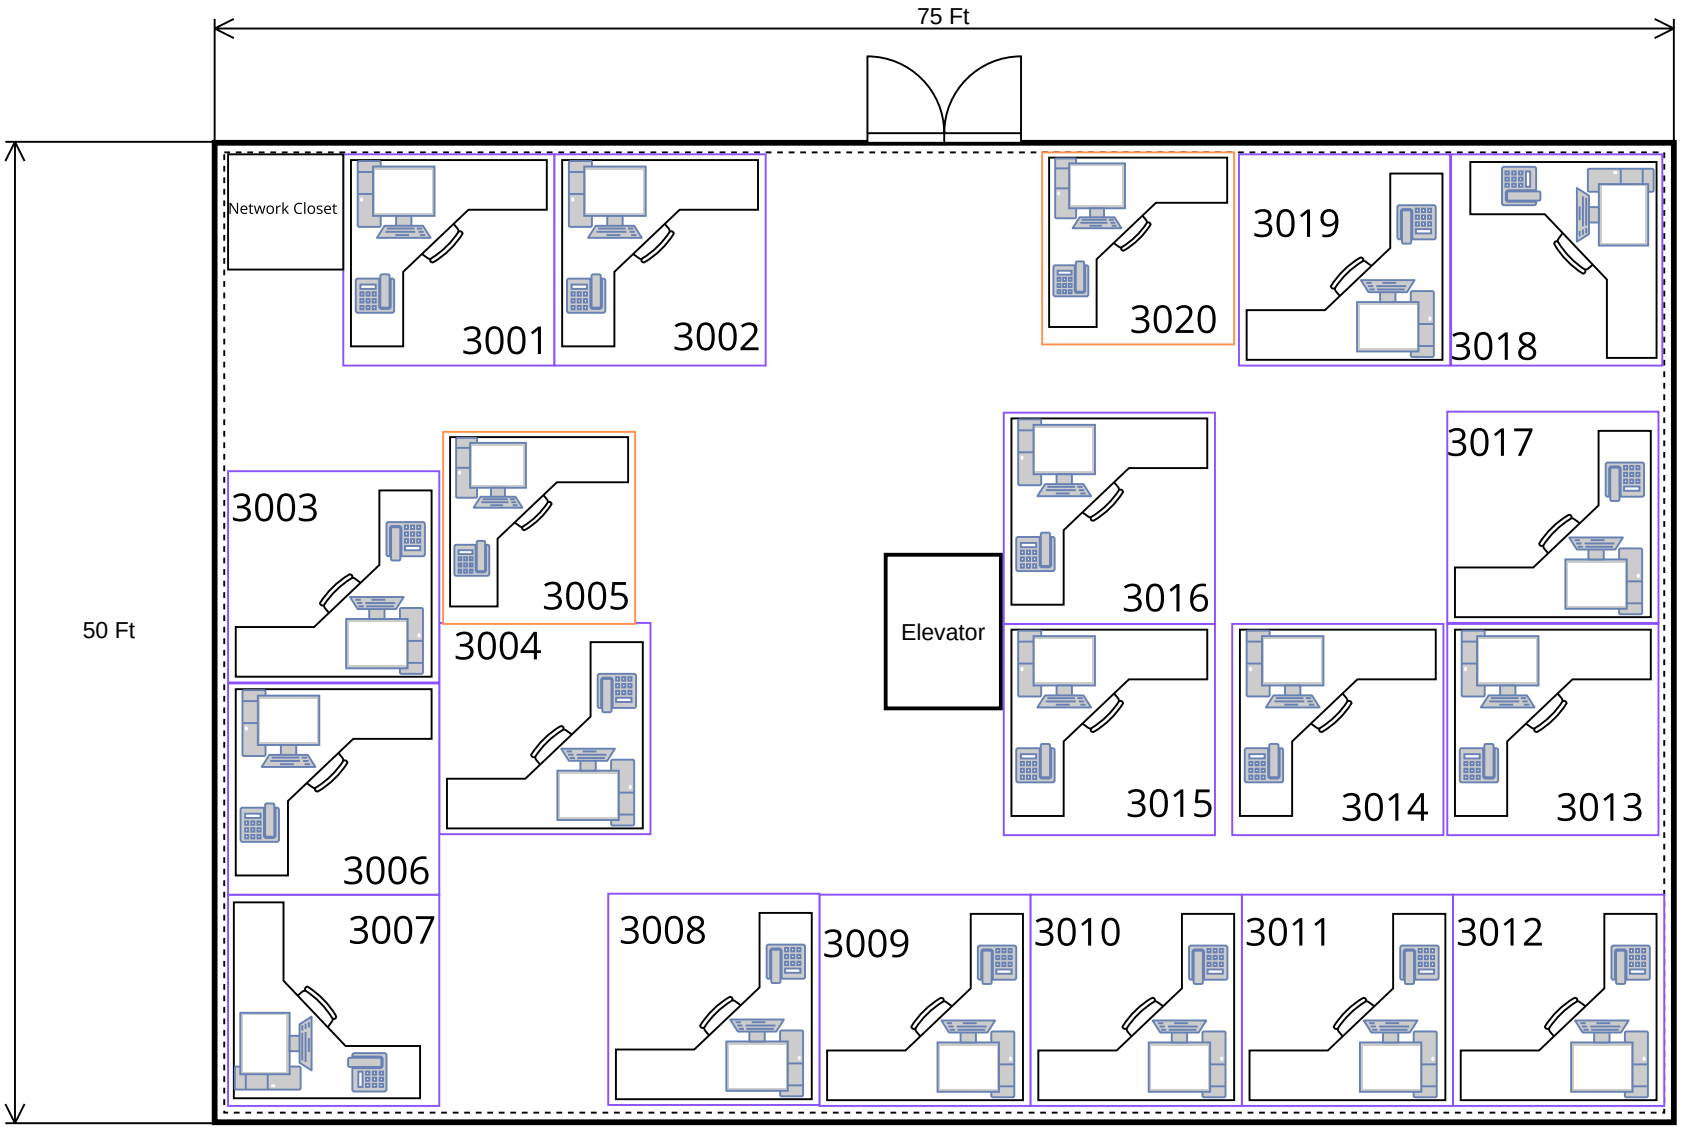

Made with Visual Paradigm
For non-commercial use

Building B Floor 2 :
Departments 3 & 4

Key :


3000 Code = Engineering Department
4000 code = Direct/Corporate Sales Department

= Support Cubicle

= Regular Cubicle

Made with VisualParadigm
For non-commercial use

Floor 2

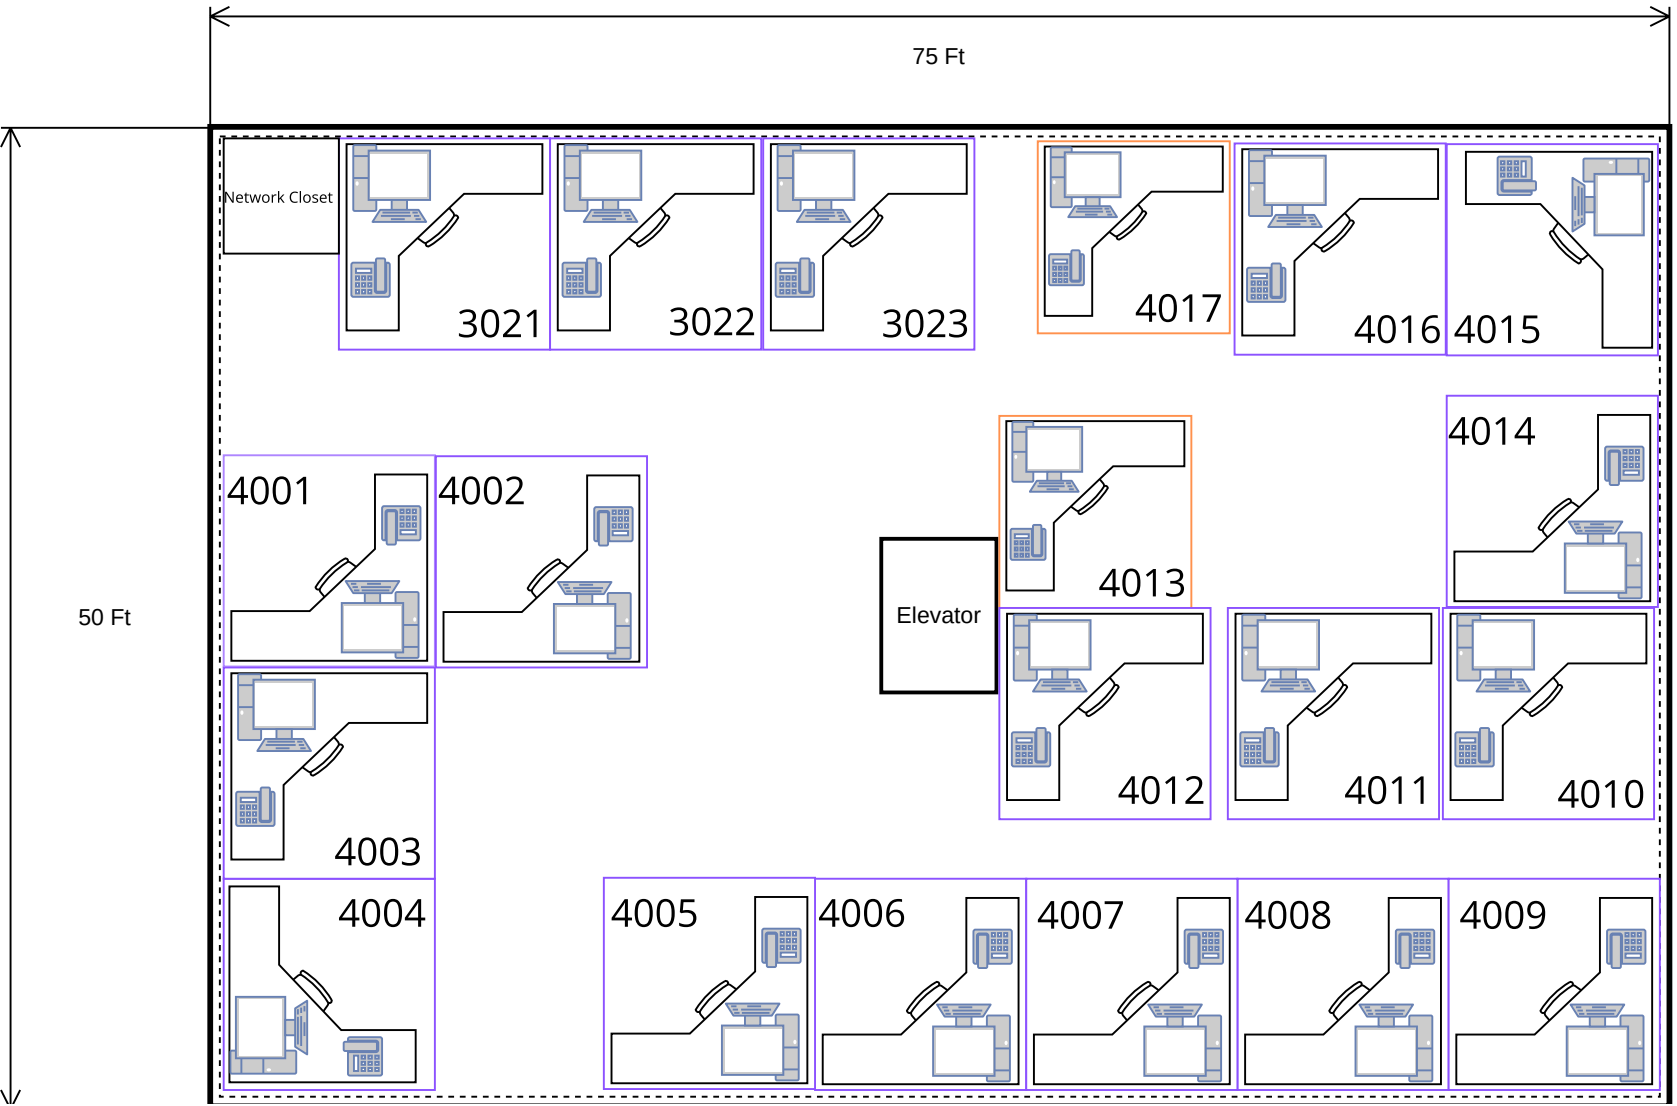

Made with
VisualParadigm
For non-commercial use

Buidling B Floor 3 :
Departments 1 & 4


Key :

1000 code = Marketing Department
4000 code = Direct/Corporate Sales Department

= Support Cubicle

= Regular Cubicle

Floor 3

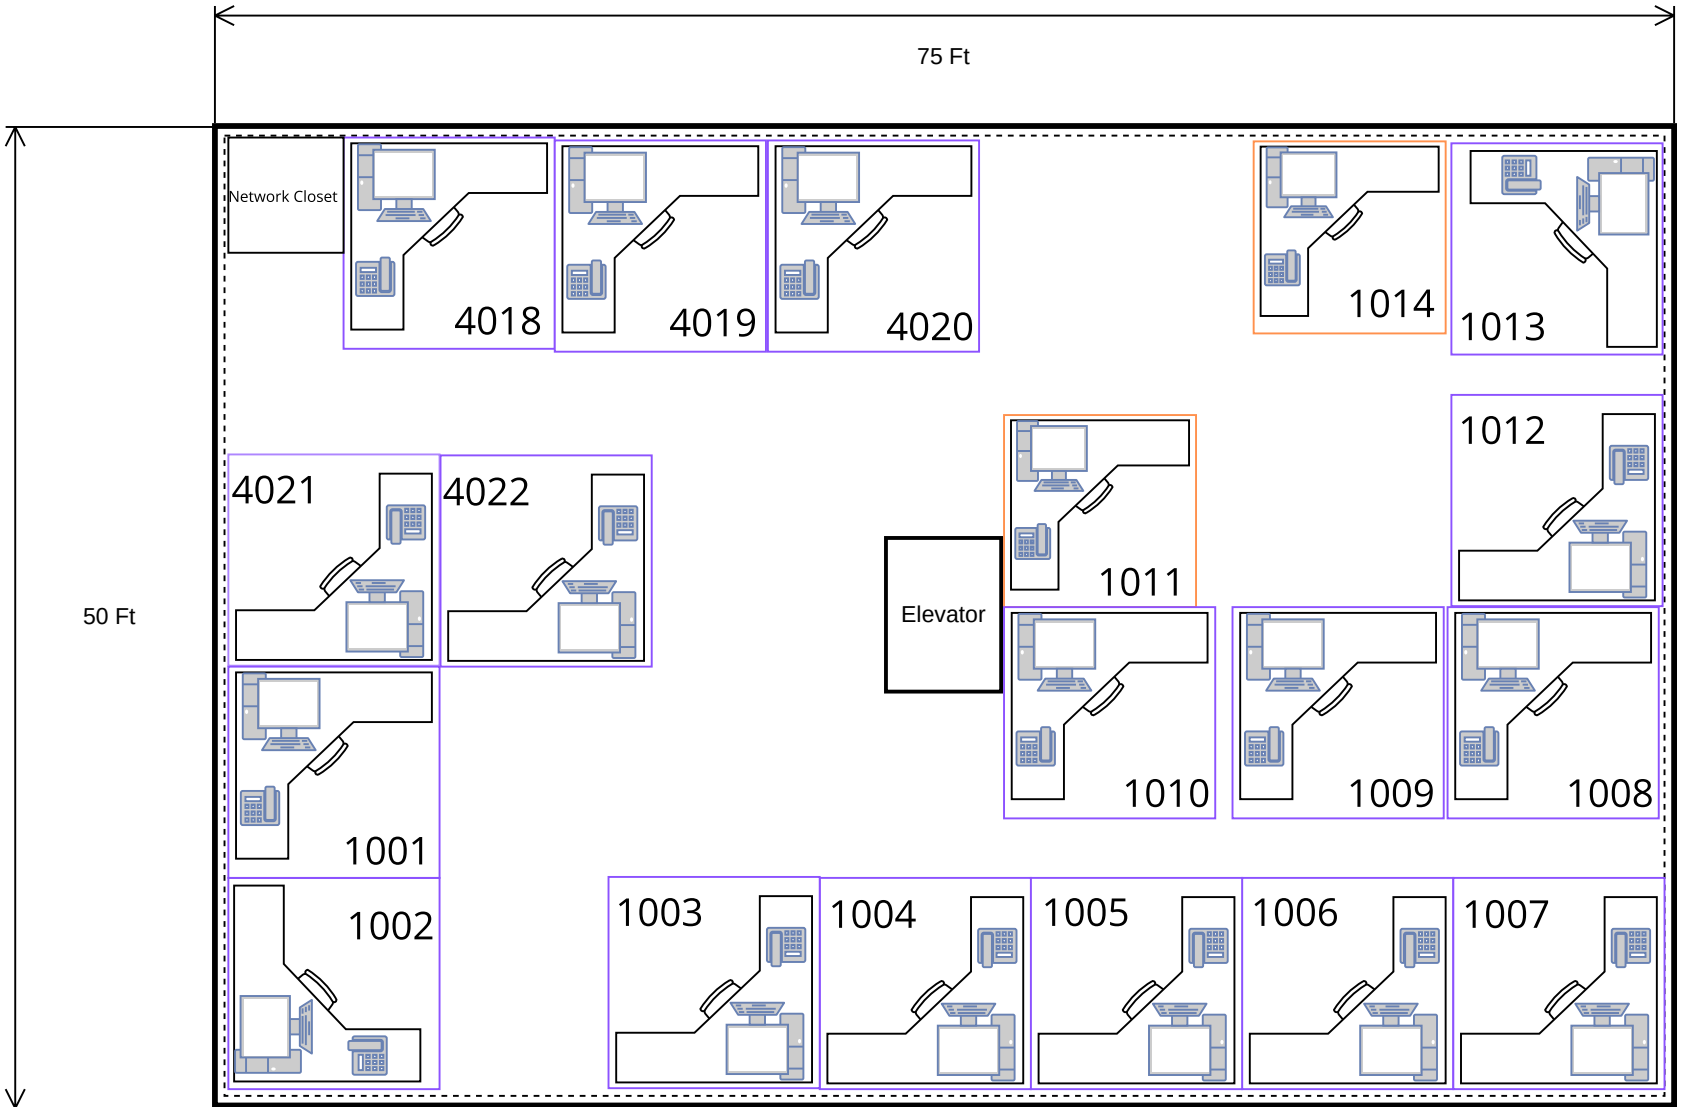

Made with
VisualParadigm
For non-commercial use

Buidling B Floor 4 :
Department 1 & 2

Key :


1000 code = Marketing Department
2000 code = Customer Support

= Support Cubicle

= Regular Cubicle

Made with Visual Paradigm
For non-commercial use

Floor 4

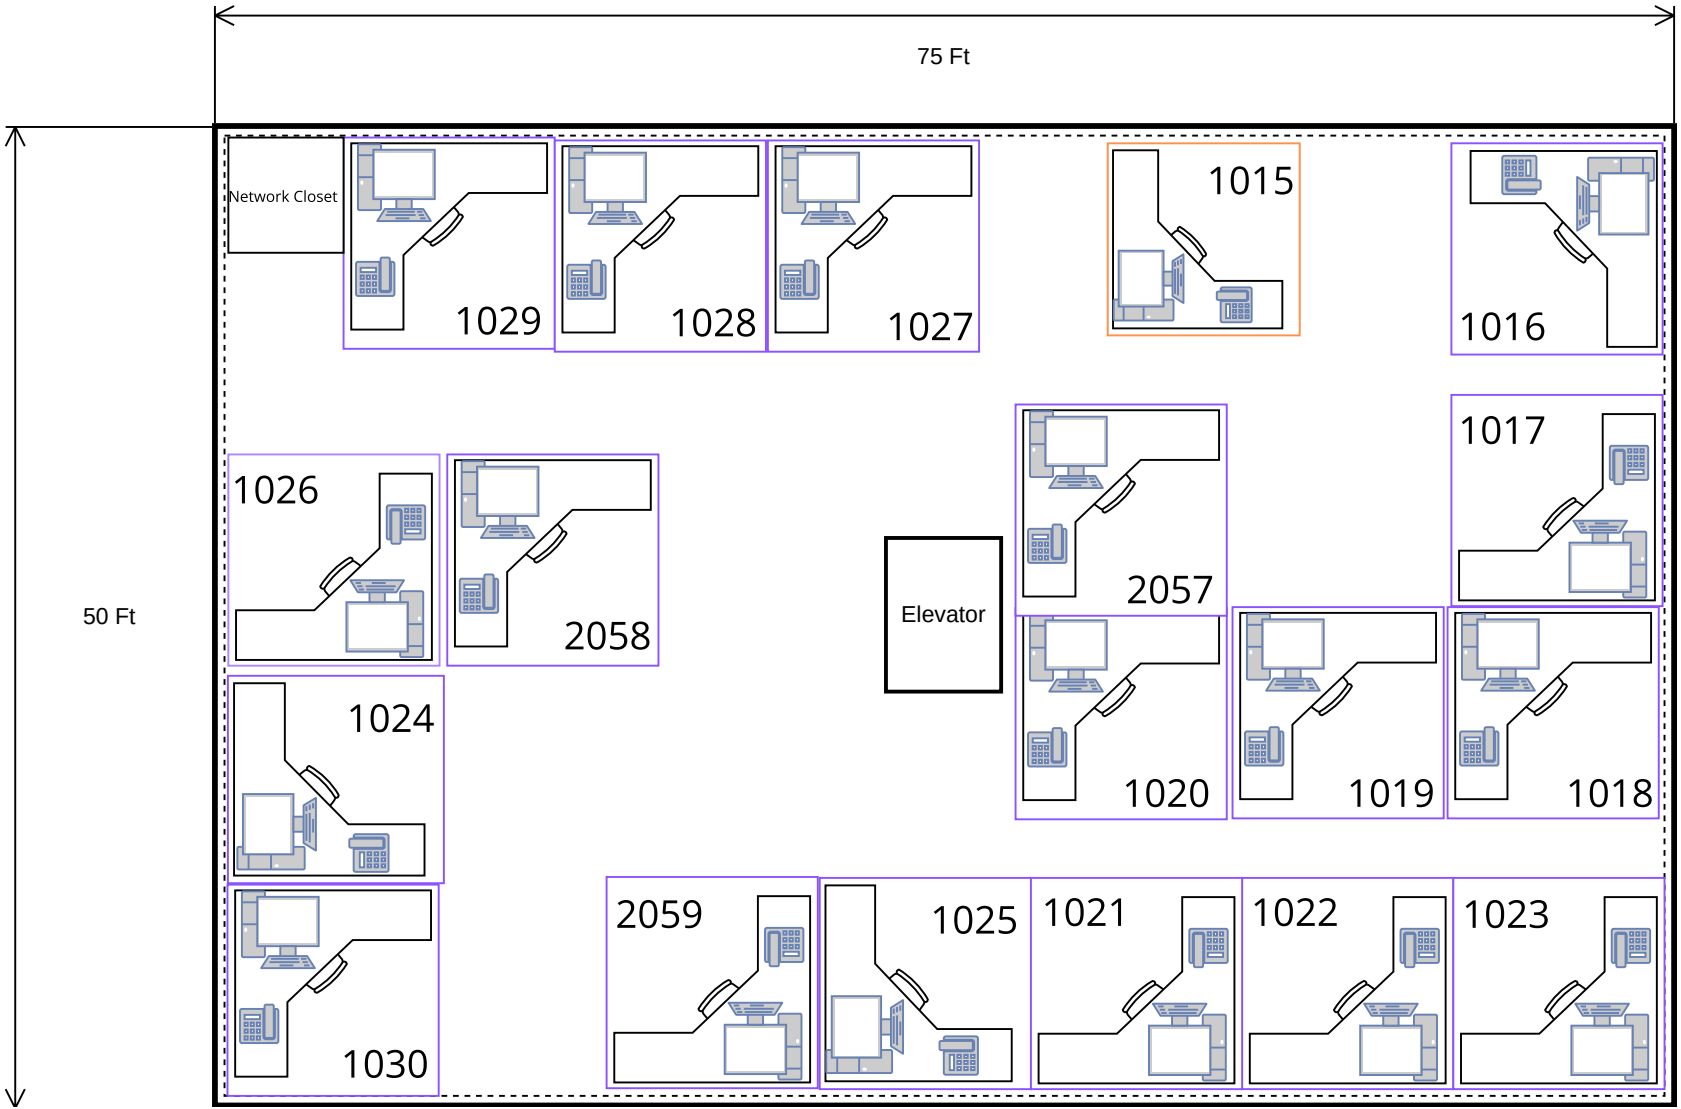

Made with
VisualParadigm
For non-commercial use

Buidling B Floor 5 :
Department 1 & 2

Key :

1000 code = Marketing Department
2000 code = Customer Support

= Support Cubicle

= Regular Cubicle

Made with Visual Paradigm
For non-commercial use

Floor 5

